


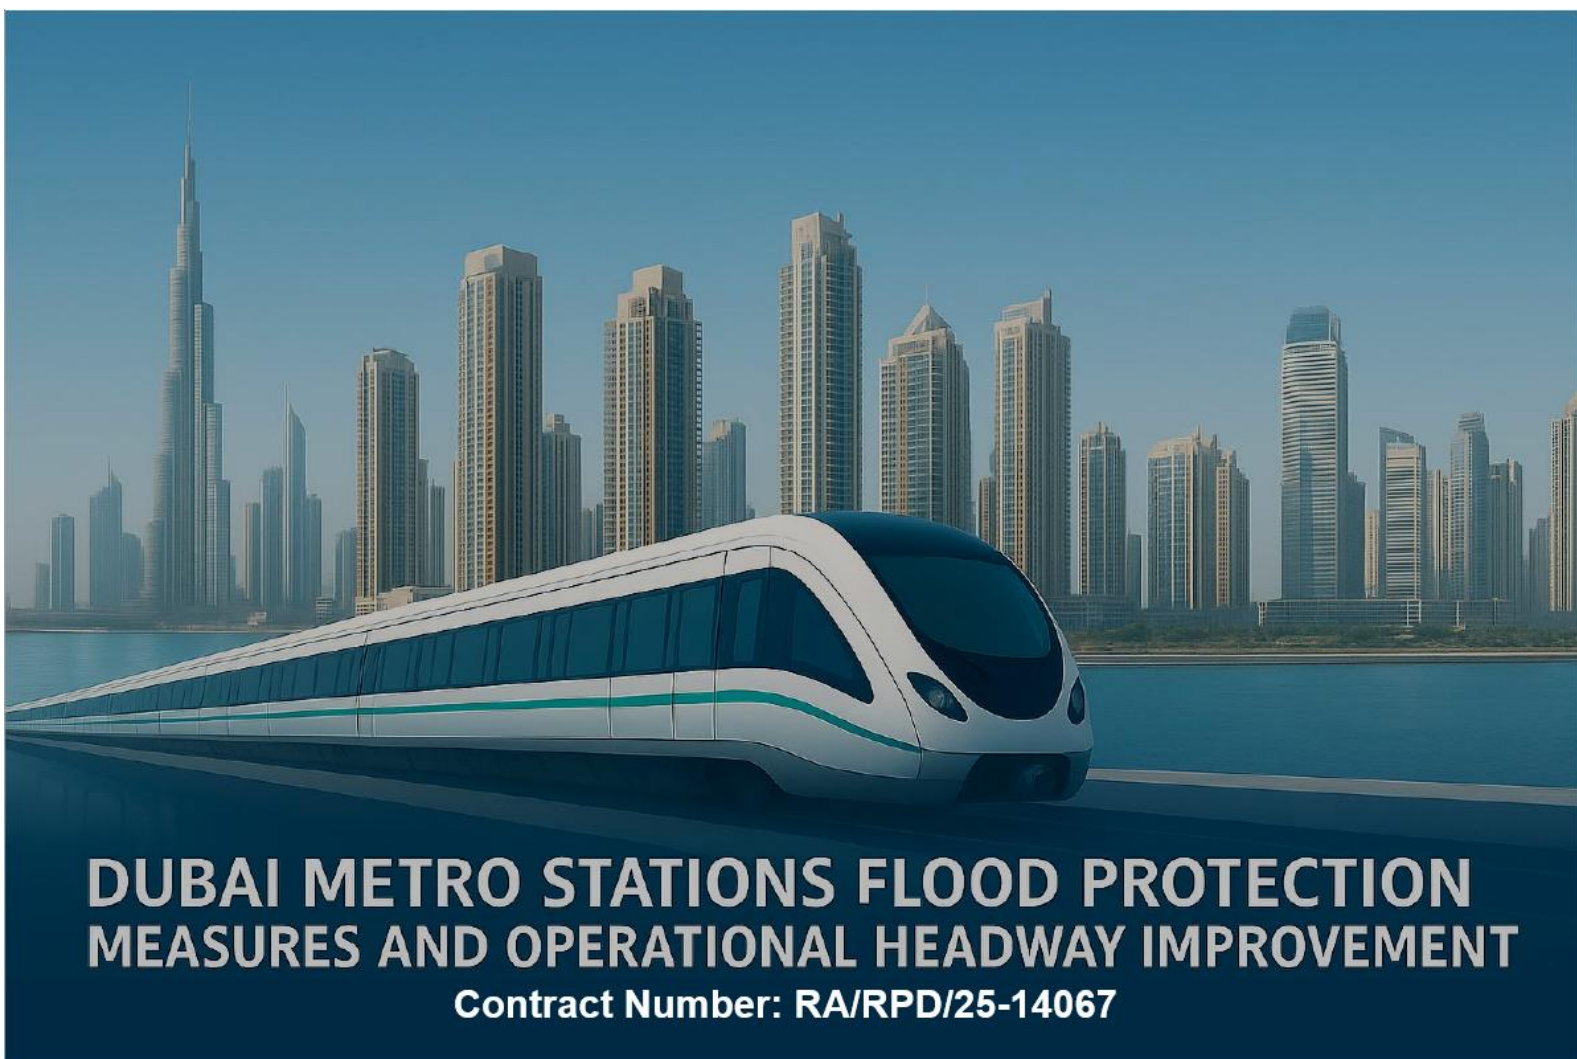

CIVIL AND STRUCTURAL

DCP1 - SITE FENCE GENERAL ARRANGEMENT

Title: DCP1 - SITE FENCE GENERAL ARRANGEMENT		
Reference : ALACO-C0000-CIV-NWW-GAR-DRW-2100001	Dubai Metro Water Flood and Operational Headway Improvement Project	Revision: 01
Owner Organization: ACO		Page: 1/3

HISTORY

		Submission:	☒ For Information Only ☐ For Approval	
Rev	Date	Modifications (Chapter / Section / Reason)	Author	Function
01	13-May-2026	First Issue	Amr Mansour	Engineering Manager

SUBMISSION LEVEL / STAGE

Design	☒ DCP1	☐ DCP2	☐ DCP3	☐ DCP4	☐ Single Submission	
Others	☐ MAN	☐ CON / INS	☐ T&C	☐ O&M	☐ DNP	☐ ASB
	☐ RAMS	☐ System Validation	☐ System Acceptance	☐ Revenue Service		

INTERNAL REVIEW

	Written by	Verified & Validated by	Approved by
Name	N/A	Amr Mansour	Mohamed Al Nakhala
Function	N/A	Engineering Manager	Project Manager
Date	N/A	13-06-2026	13-06-2026
Signature	N/A		

CONSORTIUM REVIEW AND APPROVAL

	REVIEWER 1	REVIEWER 2	REVIEWER 3	APPROVED BY
Name				RAO Rajesh
Function, Entity				Project Director, ALS-ACO
Date				13-06-2026
Signature				

Title: DCP1 - SITE FENCE GENERAL ARRANGEMENT		
Reference : ALACO-C0000-CIV-NWW-GAR-DRW-2100001	Dubai Metro Water Flood and Operational Headway Improvement Project	Revision: 01
Owner Organization: ACO		Page: 2/3


DRAWINGS AND DOCUMENTS ATTACHED

Sl.	Drawing No	Drawing Title	Rev
1	ALACO-C0000-CIV-NWW-GAR-DRW-2100001	SITE FENCE GENERAL ARRANGEMENT	01


Title: DCP1 - SITE FENCE GENERAL ARRANGEMENT		
Reference : ALACO-C0000-CIV-NWW-GAR-DRW-2100001	Dubai Metro Water Flood and Operational Headway Improvement Project	Revision: 01
Owner Organization: ACO		Page: 3/3



KEY PLAN

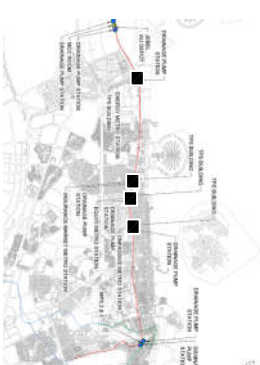


LEGEND : GENERAL

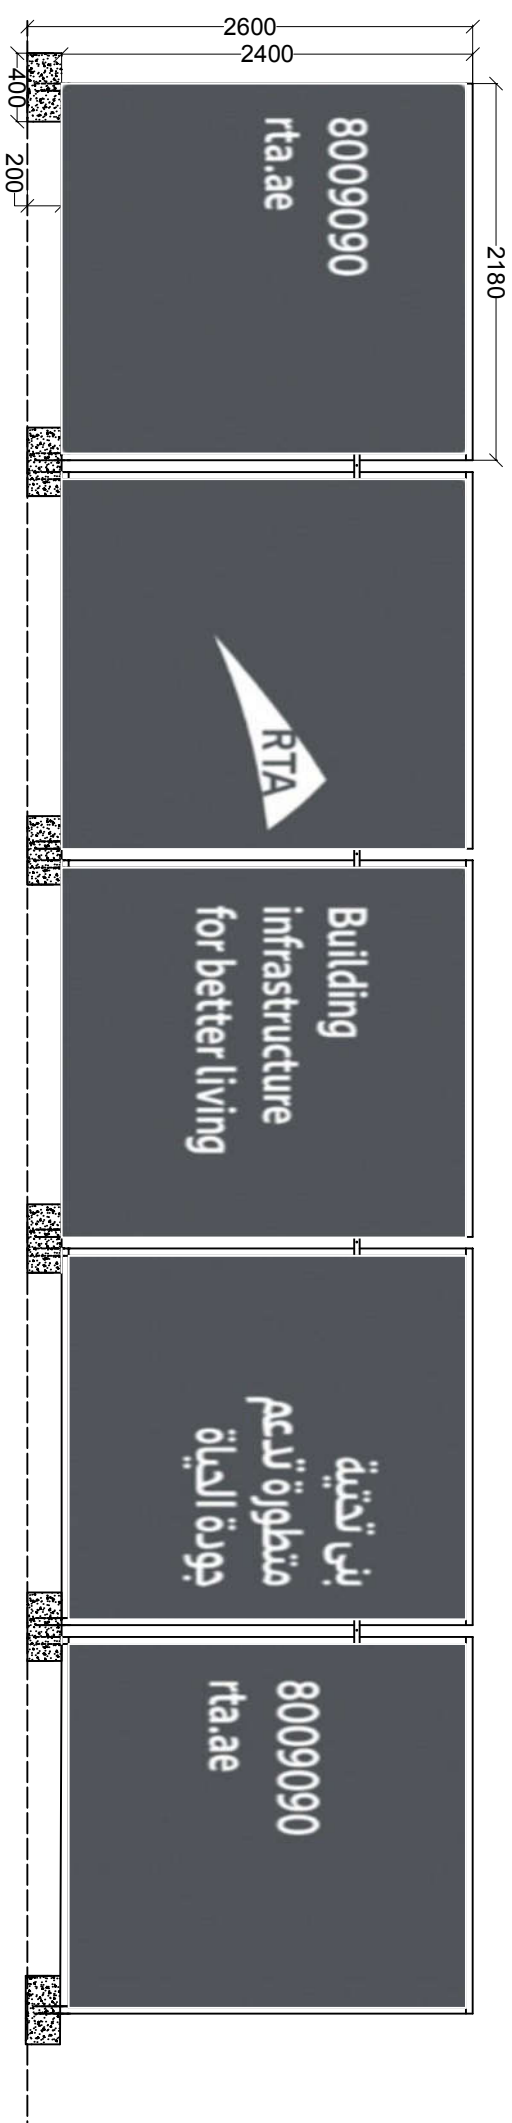

FRONT ELEVATION

ITEM	Description	Material Grade	Size / Diameter	Thickness
1	PPGI Corrugated Sheet (35/200 Profile)	ASTM A653 / PPGI	1000 mm (W) × 2400 mm (H)	0.70 mm
2	Side Support GI Pipe	GI CS Type B	42 mm OD × 2600 mm (H)	1.8 mm
3	Back Support GI Pipe	GI CS Type B	42 mm OD × 2767 mm (L)	1.8 mm
4	U-Channel (Mill Finish)	GI	60 × 48 × 60 mm	1.8 mm
5	Clamps	GI	Standard	-
6	Bolt, Nut & Washer	GI	M10 × 40 mm	-
7	Concrete Foundation Block	C40/20 Ready Mix	600 × 400 × 200 mm	-
8	RTA Flex Banner	510 GSM as per RTA standard	As per RTA artwork	-

SIDE ELEVATION

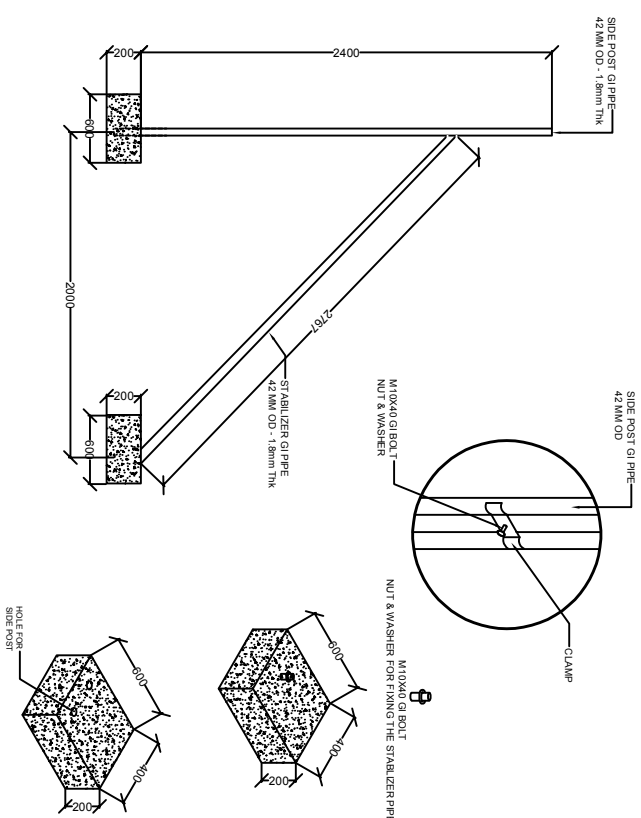

DRAFTING TITLE

SITE FENCE GENERAL ARRANGEMENT

CONTRACT NO:	RAIRP/25-14067			
DRAWN	DESIGNED	CHECKED	APPROVED	
SW	SP	ZM	ZIM	
DATE	JUNE 2026	ACTUAL SIZE	A1	
DRAWING SCALE			REV NO	
NTS				01

DRAWING NO

ALACO-C0000-CIV-NWW-GAR-DRW-210000-

CONTRACTOR



DESIGN CONSULTANT



PROJECT / CONTRACT
DUBAI METRO STATIONS
FLOOD PROTECTION MEASURES AND
OPERATIONAL HEADWAY IMPROVEMENT

SUB-CONTRACTOR



DRAWING TITLE

SITE FENCE GENERAL ARRANGEMENT

CONTRACT NO:	RAIRP/25-14067			
DRAWN	DESIGNED	CHECKED	APPROVED	
SW	SP	ZM	ZIM	
DATE	JUNE 2026	ACTUAL SIZE	A1	
DRAWING SCALE			REV NO	
NTS				01

DRAWING NO

ALACO-C0000-CIV-NWW-GAR-DRW-210000-